
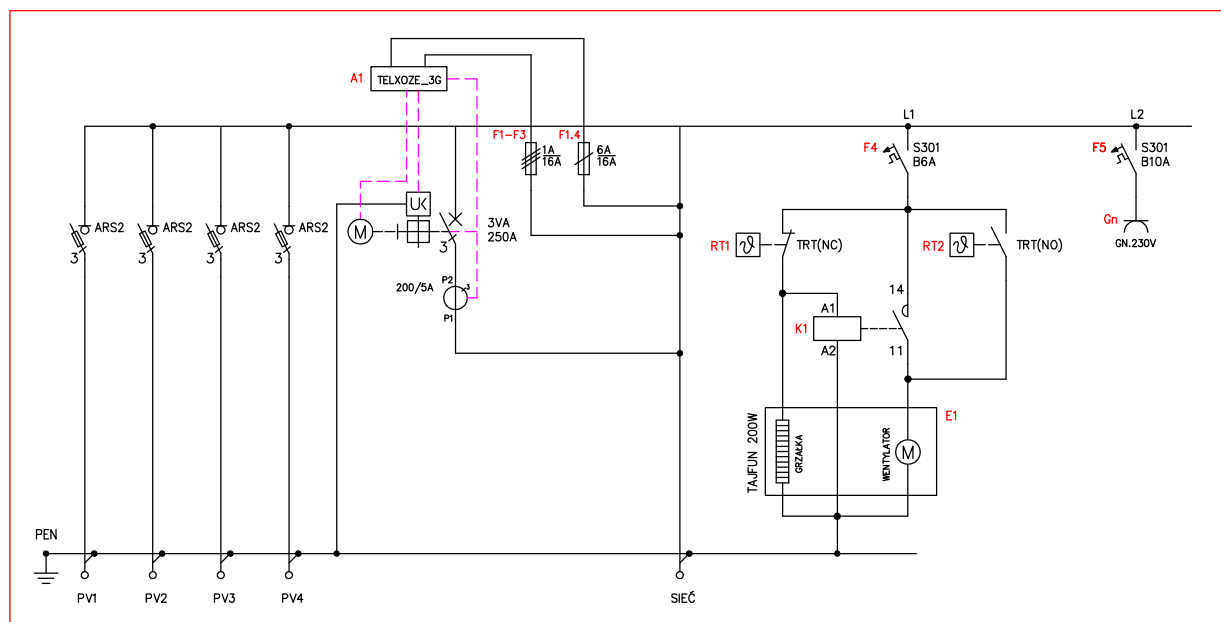


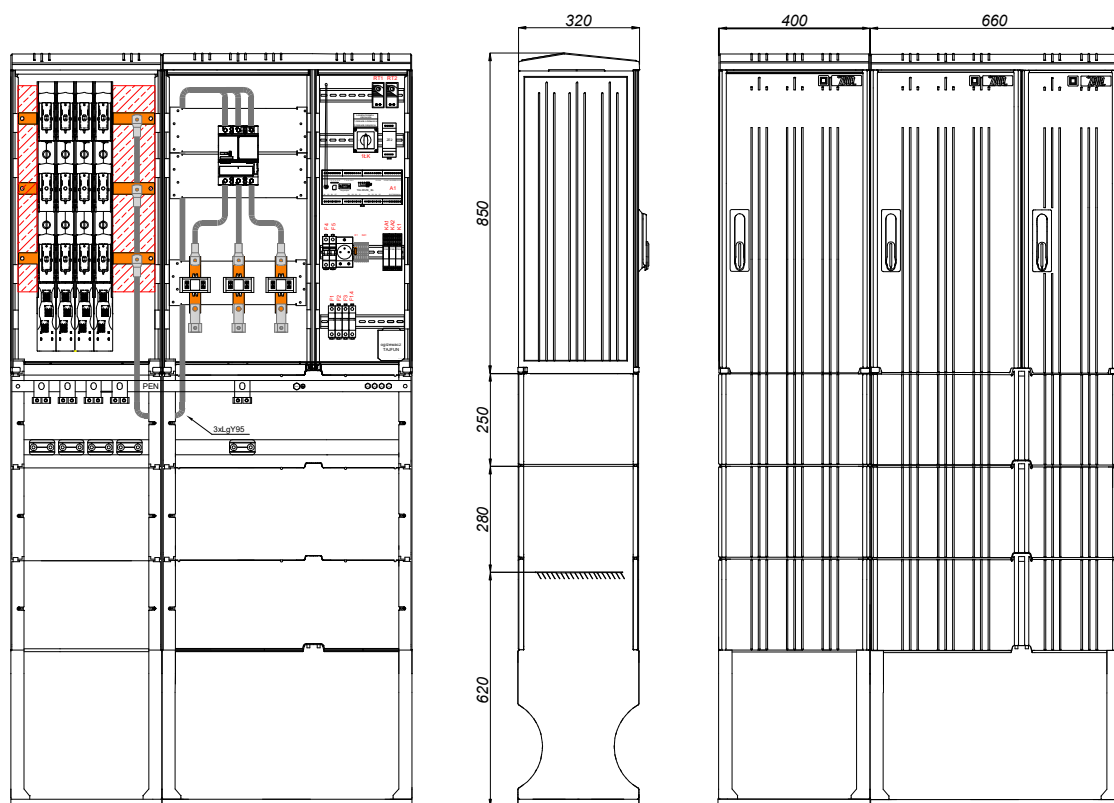

Uwaga! Opracowanie to jest tylko koncepcją do akceptacji.
OBUDOWA: SKRF 260/800/1/320+660/800/2/320+NDC

	Inwestor:		Objekt:		Format:	A4
	Przedmiot opracowania:		Nazwa rysunku:		Skala:	1:20
	Złącze kablowo-pomiarowe ZKPP OZE 200 kW		Rzuty obudowy oraz schemat ogólny		Data:	
	Opracował:	Modyfikował:	Sprawdził:	Nr. rys.:		
	inż. Piotr Grzybek			Nr. opracowania:		

Q1-Wyłącznik 3VA(Siemens)

Opis sygnałów:

X1/L+ - NAFED - ZBROJENIE

X1/L- - WYŁĄCZ

X1/OFF - WYŁĄCZ


X1/ON - ZALĄCZ

Lokaina blokada sterowania
1-blokada odsławiona
2-blokada załączona

- Ważenia sterownika:
- WYŁĄCZNIK WYZWOLOWY (TAS-1-4)
 - WYŁĄCZNIK ZALĄCZONY (AUX-1-4)
 - WYŁĄCZNIK WYŁĄCZONY (AUX-1-2)
 - LOKALNA BLOKADA STEROWANIA ZALĄCZONA
 - BLOKADA STEROWANIA

Łącznik TLK:

- LOKALNA BLOKADA STEROWANIA ODSŁAWIONA
- LOKALNA BLOKADA STEROWANIA ZALĄCZONA

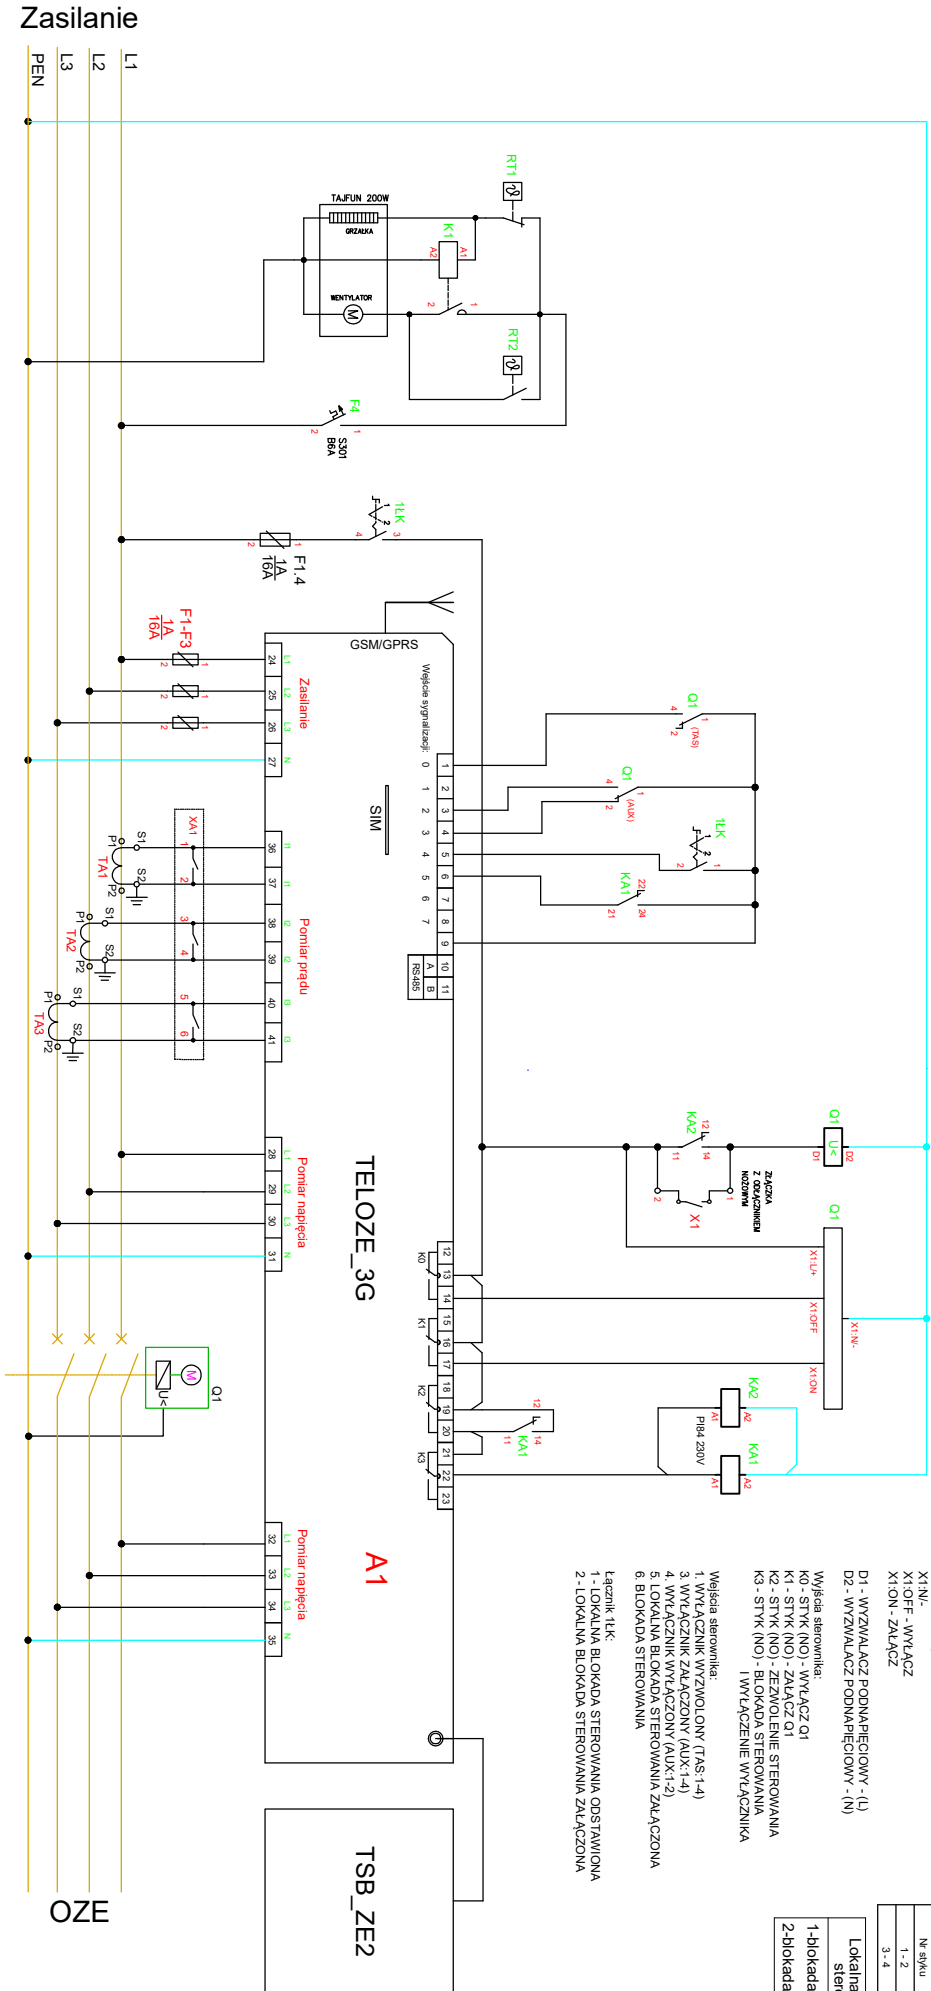




Zasilanie

OZE

Uwaga! Opracowanie to jest tylko koncepcją do akceptacji.

Investor:		Obiekt:	
Przedmiot opracowania:		Nazwa rysunku:	
Złącze kablowo-pomiarowe		Schemat elektryczny	
ZKPP OZE 200 kW		Nr. rys.:	
Opracował:		Sprawdził:	
inż. Piotr Grzybek		Nr. opracowania:	



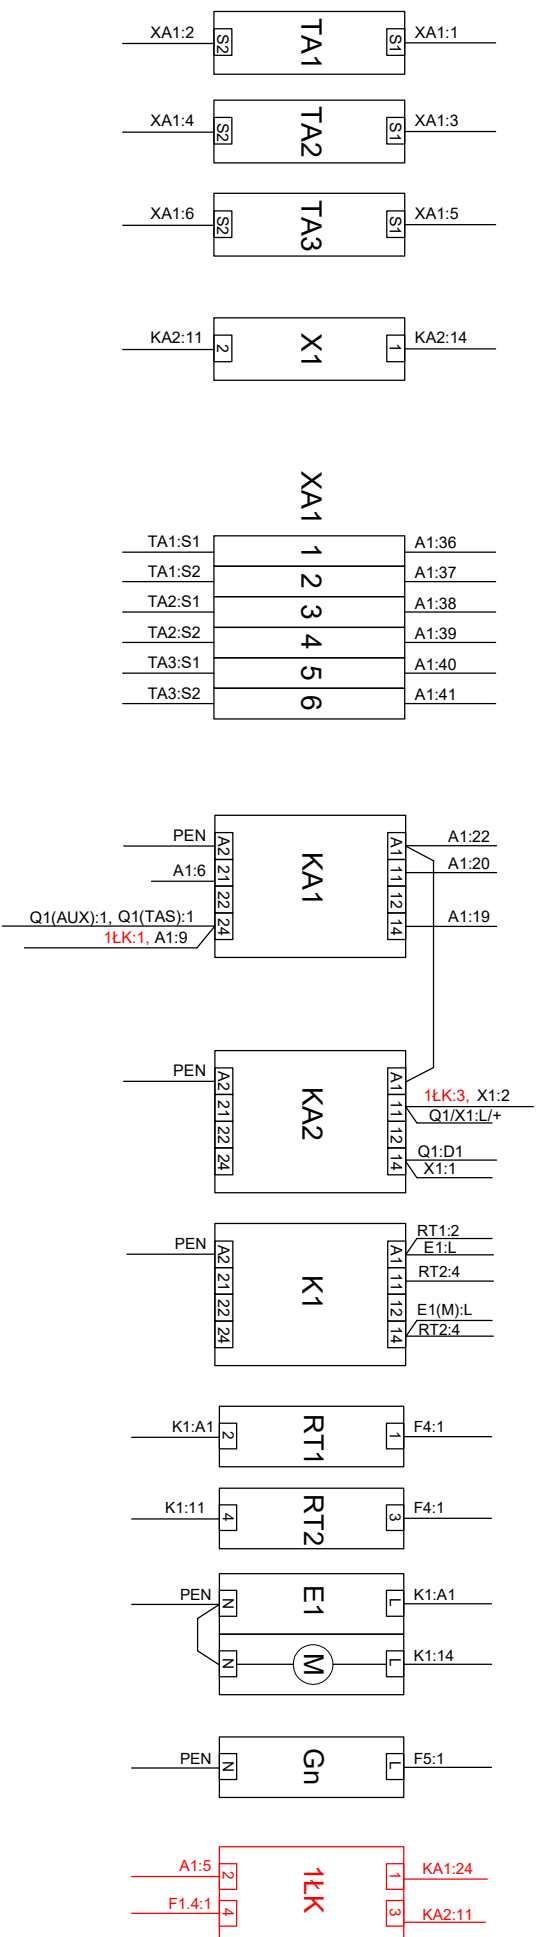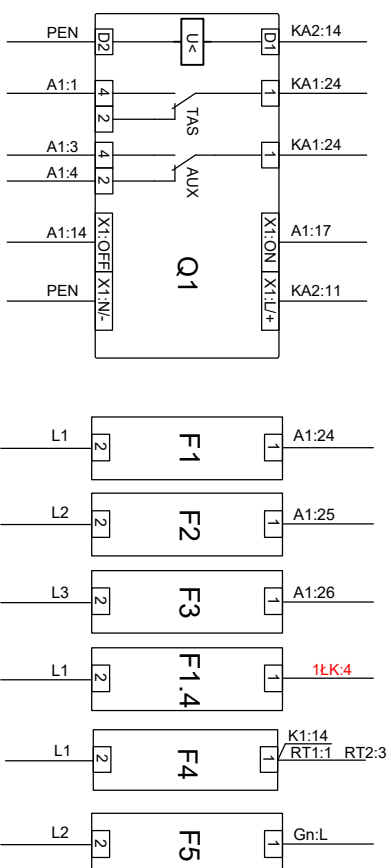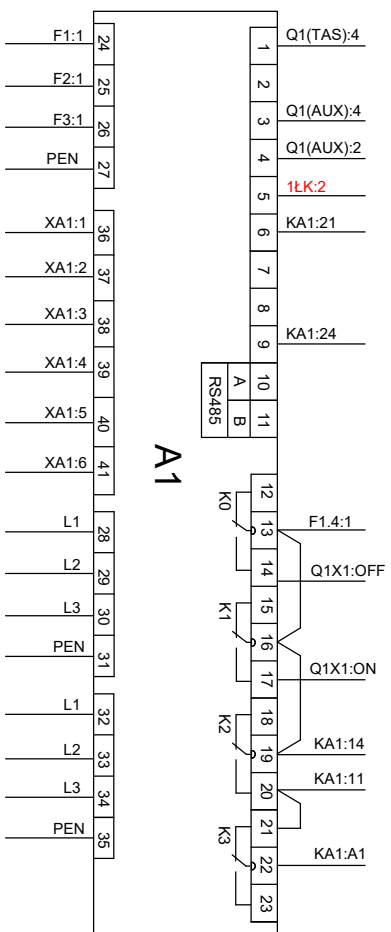

Uwaga! Opracowanie to jest tylko koncepcją do akceptacji.



Investor:

Obiekt:

Format:	A4
---------	----

Skala:

Przedmiot opracowania:

Nazwa rysunku:

Data:

Złącze kablowo-pomiarowe
ZKPP OZE 200 kW

Oznaczenia układu połączeń

Nr. rzs.:

Modyfikować:

Sprawdził:

Nr. opracowania:

inż. Piotr Grzybek