

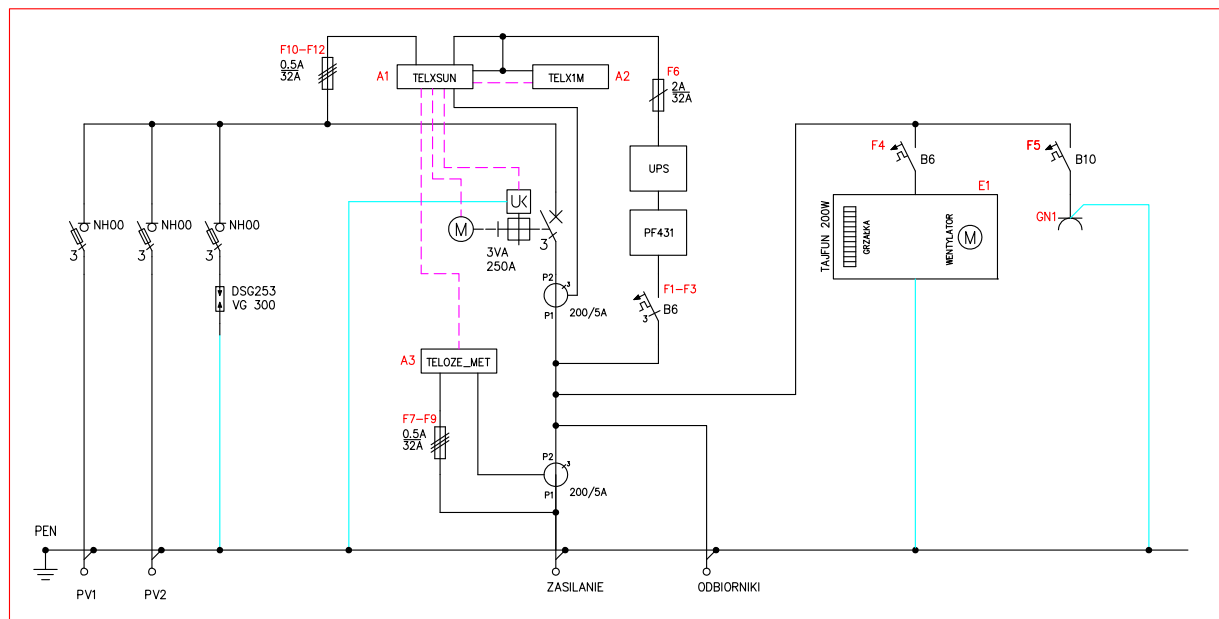


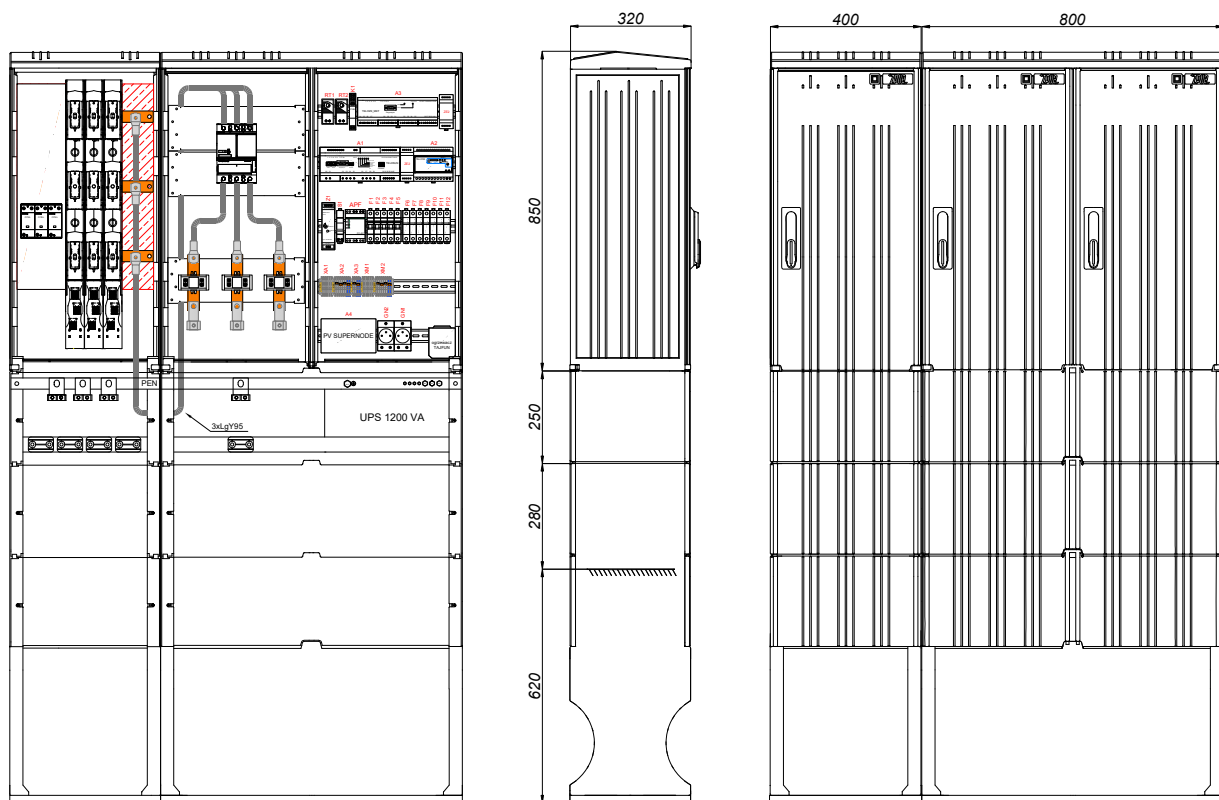

	Inwestor:		Obiekt:		Format:	A4
					Skala:	1:20
	Przedmiot opracowania: Złącze kablowo-pomiarowe ZKPP OZE 200 kW		Nazwa rysunku: Rzuty obudowy oraz schemat ogólny		Data:	
					Nr. rys.:	
	Opracował:	Modyfikował:	Sprawdził:	Nr. opracowania:		
	inż. Piotr Grzybek					

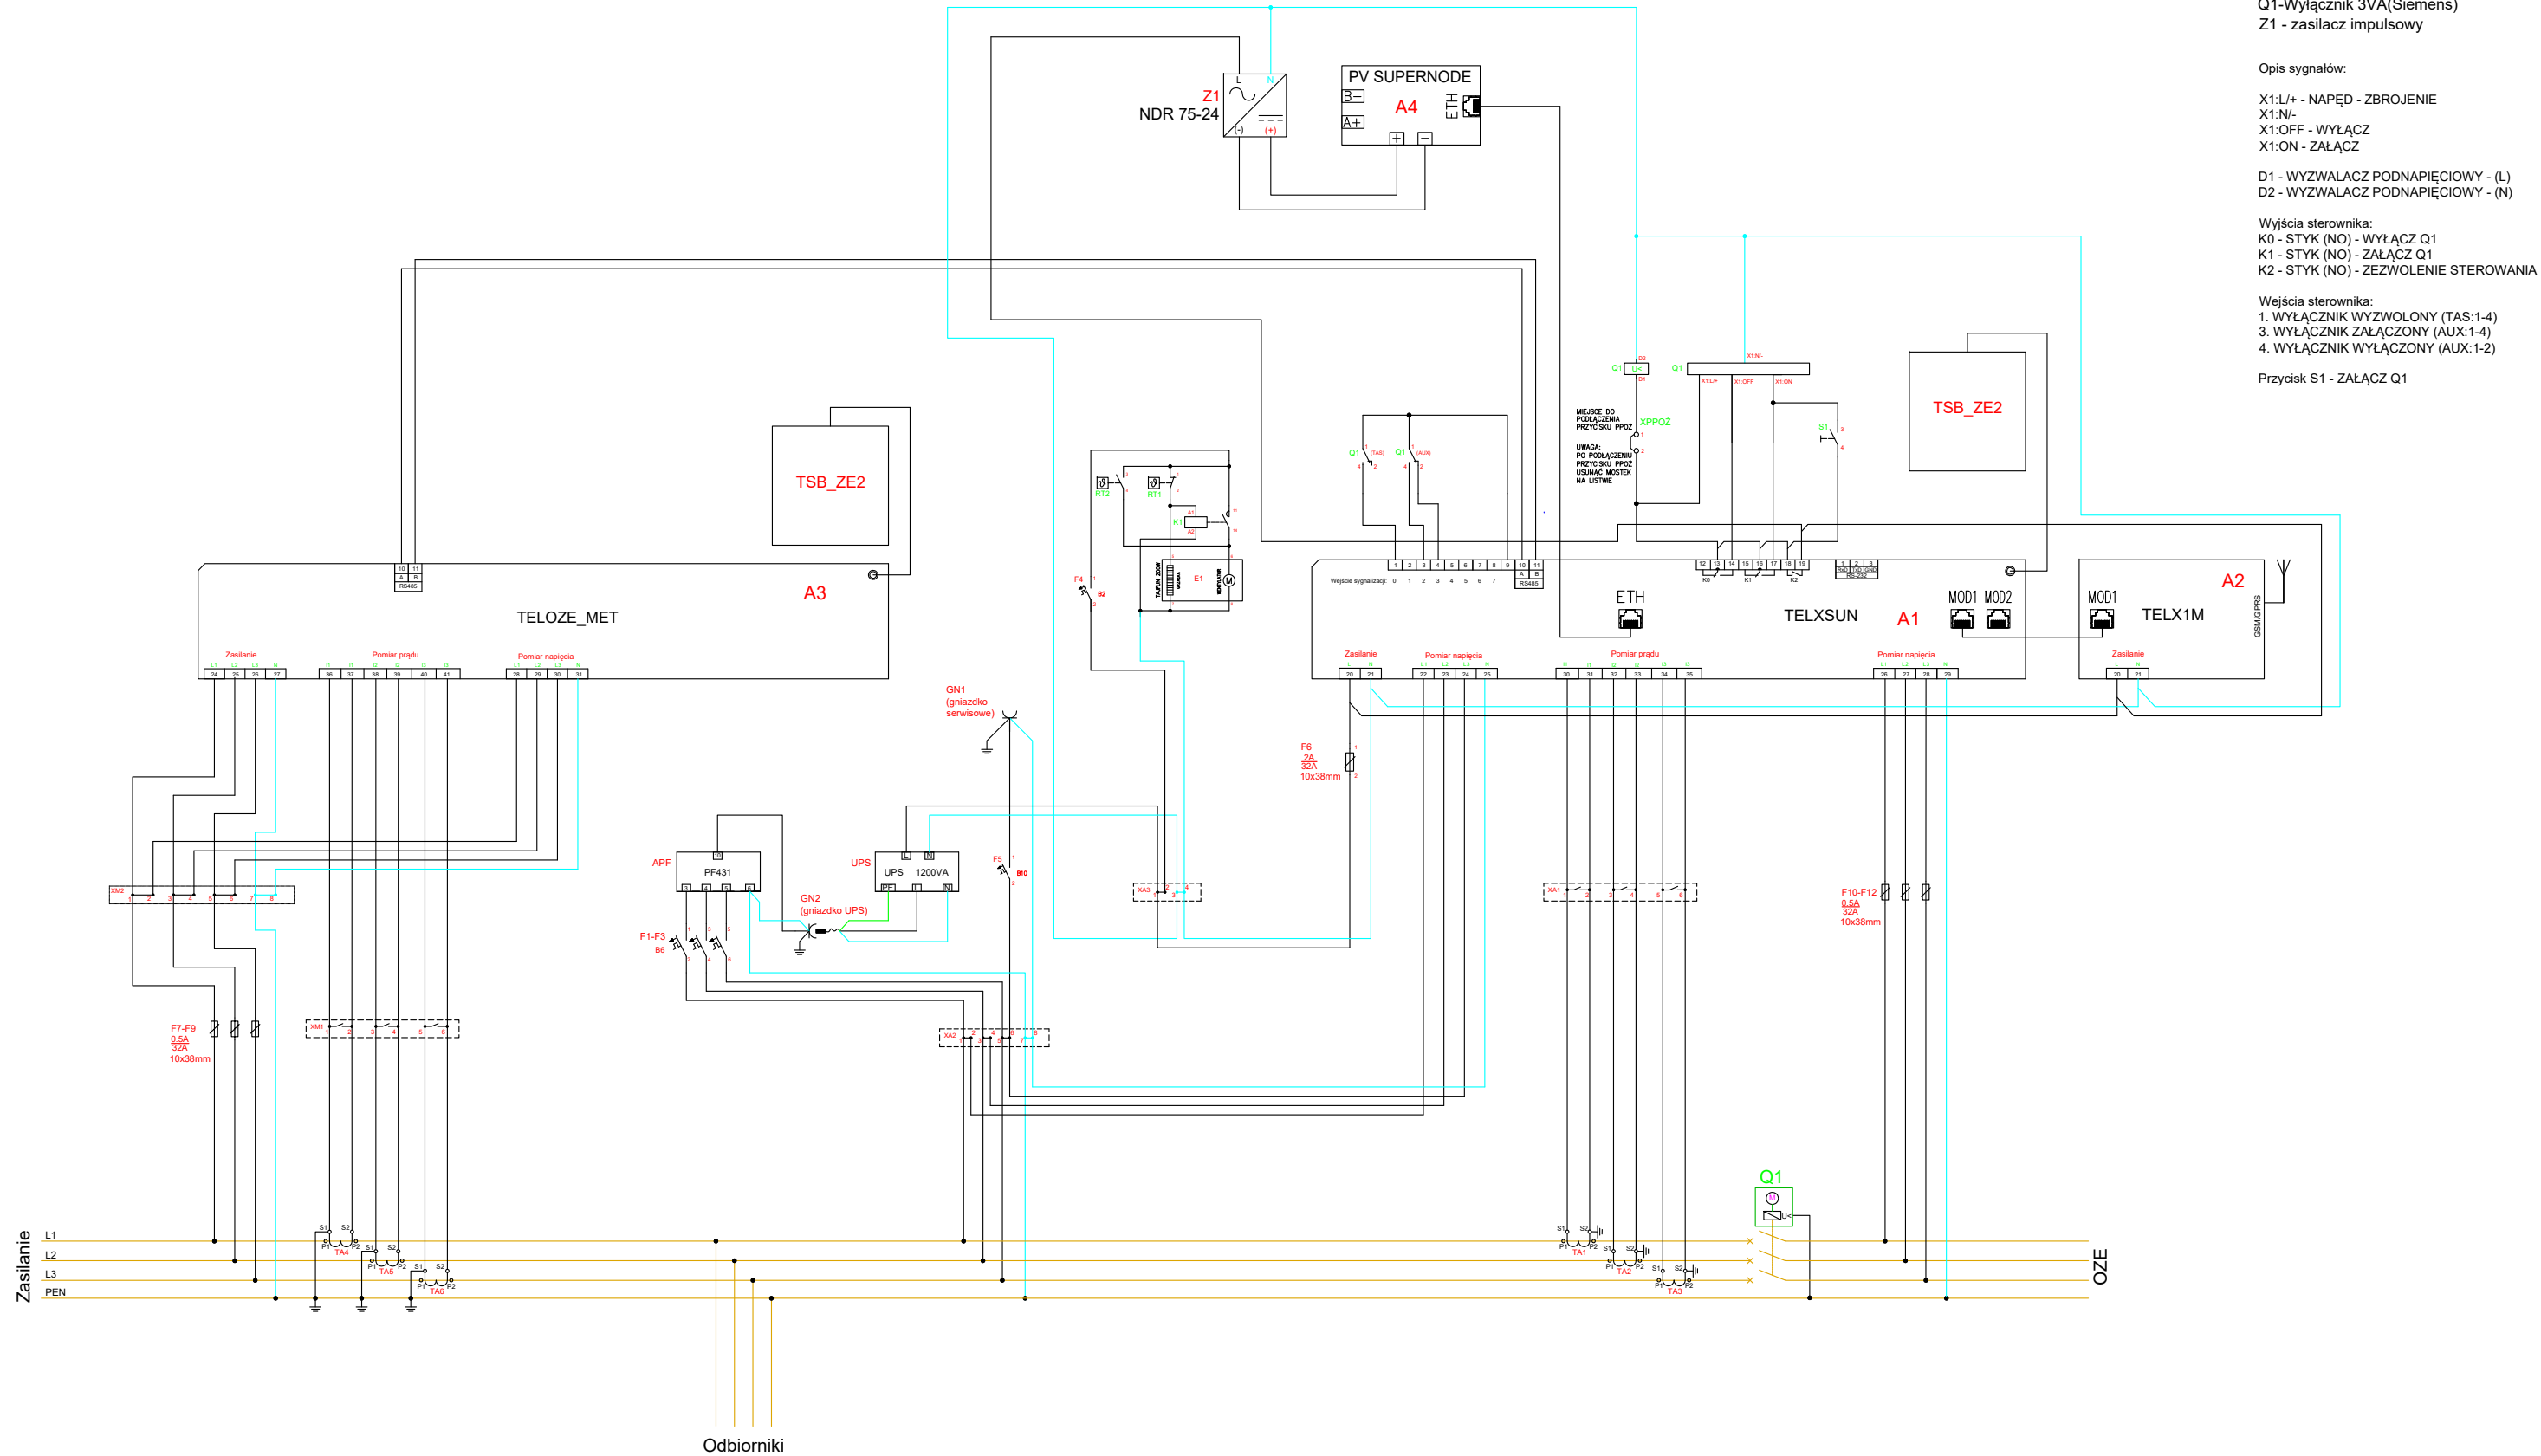

- Q1-Wyłącznik 3VA(Siemens)
Z1 - zasilacz impulsowy
- Opis sygnałów:
- X1:L/+ - NAPĘD - ZBROJENIE
X1:N/-
X1:OFF - WYŁĄCZ
X1:ON - ZAŁĄCZ
- D1 - WYZWALACZ PODNAPIĘCIOWY - (L)
D2 - WYZWALACZ PODNAPIĘCIOWY - (N)
- Wyjścia sterownika:
K0 - STYK (NO) - WYŁĄCZ Q1
K1 - STYK (NO) - ZAŁĄCZ Q1
K2 - STYK (NO) - ZEZWOLENIE STEROWANIA
- Wejścia sterownika:
1. WYŁĄCZNIK WYZWOLONY (TAS:1-4)
3. WYŁĄCZNIK ZAŁĄCZONY (AUX:1-4)
4. WYŁĄCZNIK WYŁĄCZONY (AUX:1-2)
- Przycisk S1 - ZAŁĄCZ Q1

	Inwestor:		Obiekt:		Format:	A4
	Przedmiot opracowania:		Nazwa rysunku:		Skala:	
	Złącze kablowo-pomiarowe		Oznaczenia układu połączeń		Data:	
	ZKPP OZE 200 kW				Nr. rys.:	
	Opracował:	Modyfikował:	Sprawdził:	Nr. opracowania:		

inż. Piotr Grzybek